PLANO DE SUBDIVISIÓN

SITUACIÓN PROPUESTA
ESCALA : 1 / 1.000

SITUACIÓN ACTUAL
ESCALA : 1 / 2.000

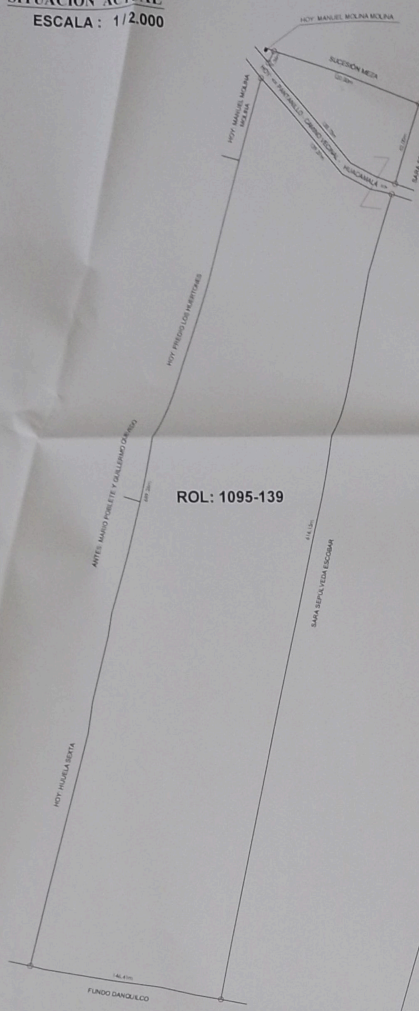

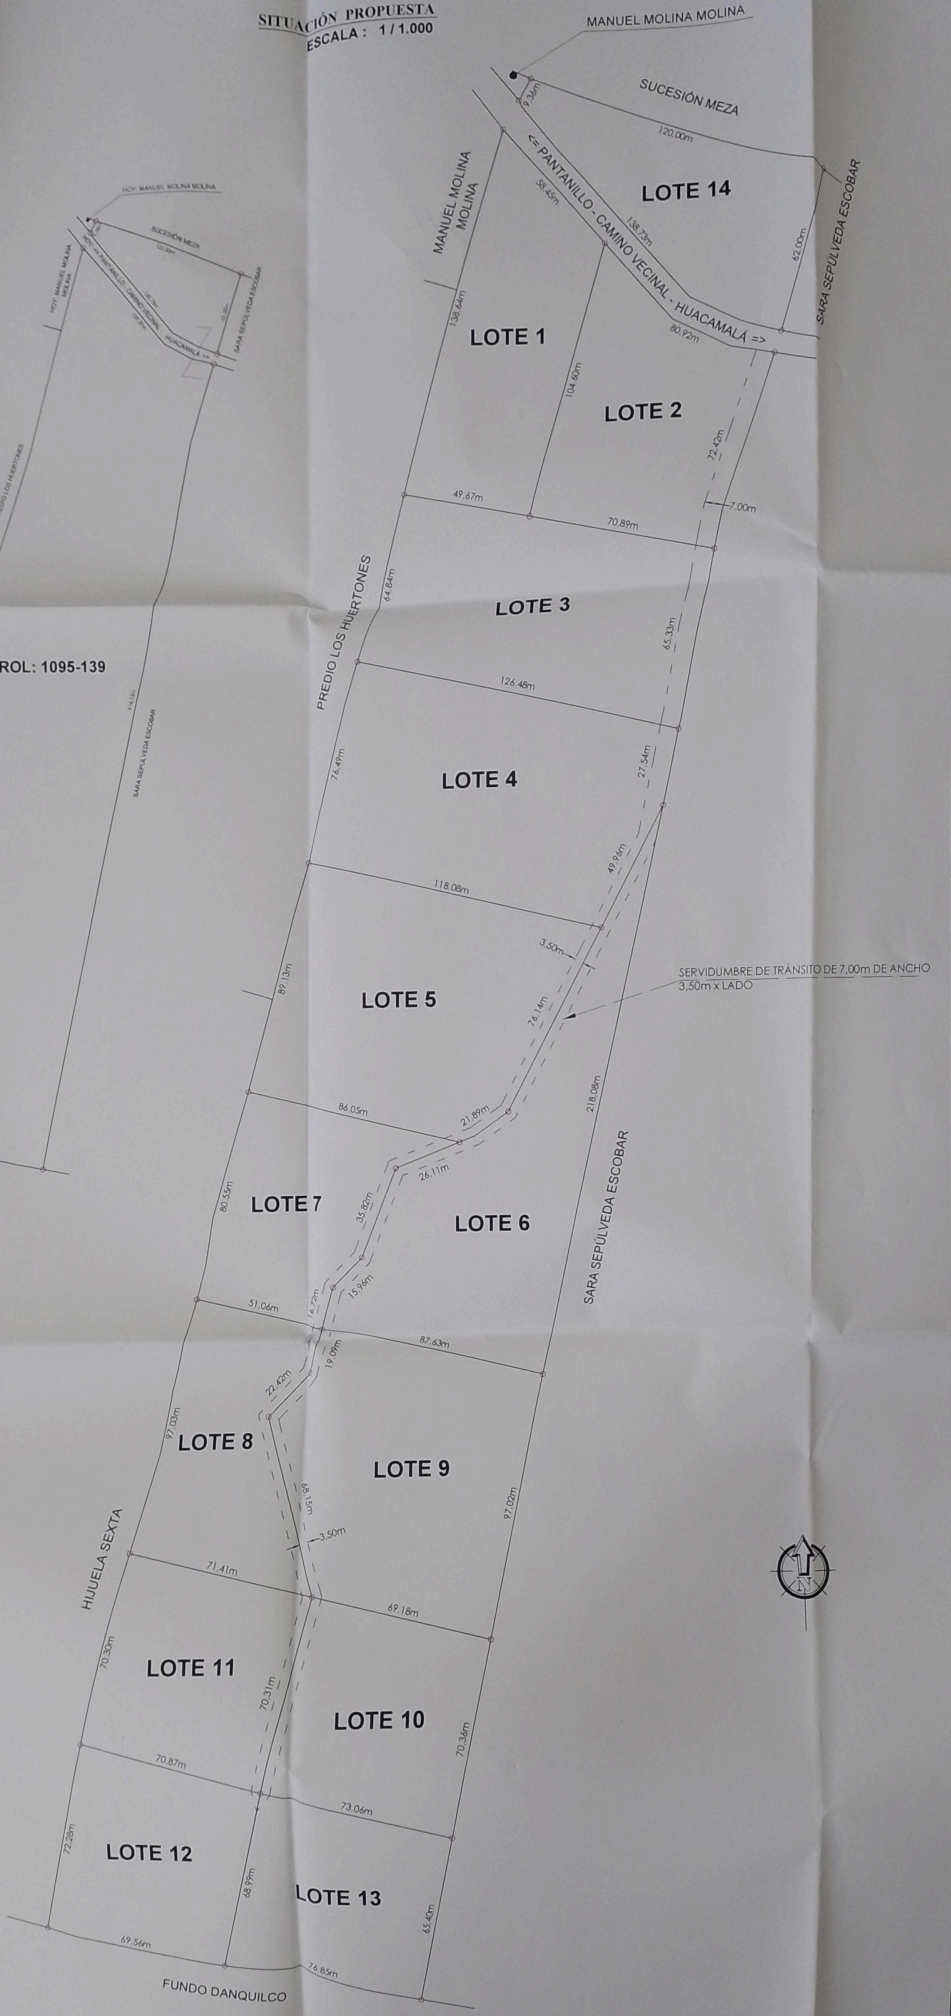

El Servicio Agrícola y Ganadero certifica que los lotes resultantes de la subdivisión y graficados en el presente plano representan una superficie igual o inferior a 12 hectáreas no significando autorización de uso de suelos, ni validación de los antecedentes de dominio, demarcatorios o de georreferencia informados por el solicitante. Como tampoco la validación del derecho necesario para la materialización de la servidumbre eventualmente proyectada, ni del necesario para acceder a espacio público, ni la verificación de prohibiciones que el predio tenga para ser subdividido.

JEFE DE OFICINA, SECTOR ÑUBLES
REGIÓN DE ÑUBLE
CERTIFICADO N° 1230
En ÑUBLES a 16 DIC 2022
Esta certificación se invalidará automáticamente si el plano se presenta enmendado

JEFE OFICINA ÑUBLES

PLANO DE UBICACIÓN

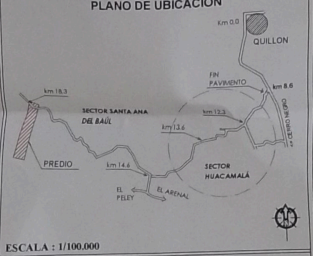

ESCALA : 1/100.000

CUADRO DE SUPERFICIES

NOMBRES	SUPERFICIE	SERV.	ANCHO
LOTE 1	0,600 HÁS		
LOTE 2	0,600 HÁS	523 m2	7,00m
LOTE 3	0,800 HÁS	457 m2	7,00m
LOTE 4	0,955 HÁS	391 m2	7m/3,5m
LOTE 5	0,955 HÁS	346 m2	3,5m
LOTE 6	0,877 HÁS	825 m2	3,5m
LOTE 7	0,500 HÁS	328 m2	3,5m
LOTE 8	0,500 HÁS	384 m2	3,5m
LOTE 9	0,853 HÁS	383 m2	3,5m
LOTE 10	0,500 HÁS	246 m2	3,5m
LOTE 11	0,500 HÁS	246 m2	3,5m
LOTE 12	0,500 HÁS	12 m2	3,5m
LOTE 13	0,500 HÁS	12 m2	3,5m
LOTE 14	0,520 HÁS		
TOTAL	9,160 HÁS	4.153 m2	

CUADRO DE FIRMAS

JORGE LUIS ALARCON MOYA
PROPIETARIO
RUT 8.075.389-6

JOSE ANGEL VELOSO LARA
TOPÓGRAFO
RUT 15.165.395-7

ANTECEDENTES DEL PREDIO

REGIÓN	REGIÓN DE ÑUBLE
PROVINCIA	PROVINCIA DE DIGUILLÍN
COMUNA	QUILLÓN
SECTOR	SANTA ANA DEL BAÚL
ROL	1095-139
SUPERFICIE	9,160 HÁS
ORIGEN	PLANIMETRICO
REFERENCIA	UTM, HUSO 18 SUR, WGS-84
FECHA	AGOSTO DEL AÑO 2022